013/2024-АР · СТАДИЯ П · ЛИСТ 01

ДЕТСКИЙ САД НА УЛ. КОЛЛЕКТИВНАЯ

16 ГРУПП 9 852 М² 89,61 × 77,30 М 2 ЭТАЖА + КРОВЛЯ 1,45 ГА

ВИЗУАЛИЗАЦИИ — В КАДРОВ · ЧЕРТЕЖИ — СТАДИЯ П, РАЗДЕЛ АР, 7 ЛИСТОВ
АЛЬБОМ ПОДГОТОВЛЕН ДЛЯ ОБСУЖДЕНИЯ С ЗАКАЗЧИКОМ · 19.10.2026

01 ОБЛОЖКА · 02 ОБЪЕКТ · 03 СИТУАЦИЯ
04 ПЛАНЫ · 05 РАЗРЕЗ И ФАСАДЫ · 06 ДВОР
07 КРОВЛЯ · 08 ЗАМЕЧАНИЯ · 09 ПРЕДЛОЖЕНИЯ

ЧТО ЗАПРОЕКТИРОВАНО

Не «сад в парке», а городской квартал с защищённым двором

Замкнутое каре 89,61 × 77,30 м. Кольцо корпусов 10–16 м, внутри — двор 3 900 м² с шестнадцатью площадками вокруг круглой площади.

Два этажа по 4,5 м и частичный третий: спортплощадки и терраса на +8,50. Подвал 2 373 м² — бассейн, ИТП, венткамеры.

«Проект держится на одном приёме: замкнутое каре с аркадой. Всё остальное — производные от него».

ПРОГРАММА

Группы	6 + 10
Бассейн, зал	109,5 м²
Музкласс / физзал	116 / 176 м²
Пищеблок	полный цикл
Медблок	с изолятором
Лестничные клетки	11

ОСИ 1–11/1, А–Ж · СЕВЕР ≈ 45°

9 852 м²
СУММАРНАЯ ПЛОЩАДЬ

16
ГРУПП

3 900 м²
ДВОР

2 373 м²
ПОДВАЛ

FIG. 01 — ВНУТРЕННИЙ ДВОР. МОЩЕНИЕ, ПЯТНАДЦАТЬ ДЕРЕВЬЕВ, ПЛОЩАДКА. КАДР СОВПАДАЕТ С ПРОЕКТОМ ПО ГАБАРИТАМ ДВОРА И РИСУНКУ ПЛОЩАДОК.

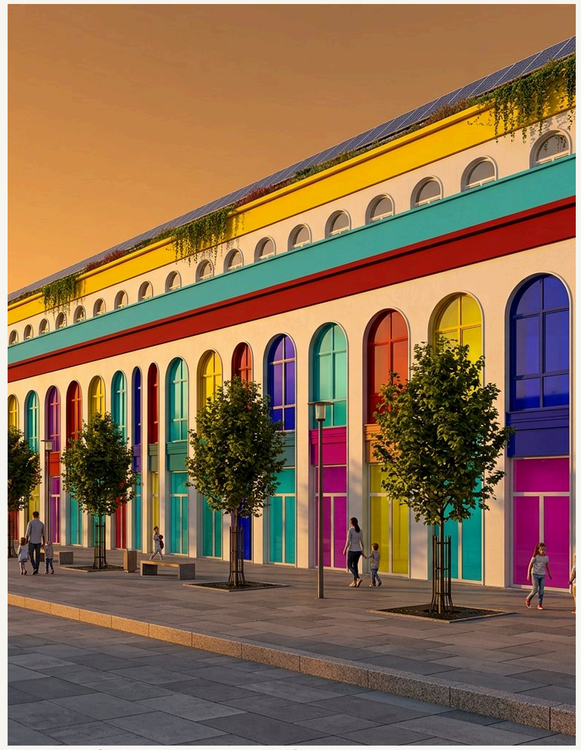

FIG. 02 — УЛИЧНЫЙ ФАСАД: АРКАДА, ДВА ЯРУСА АРОК, ЗЕЛЁНАЯ КРОВЛЯ.

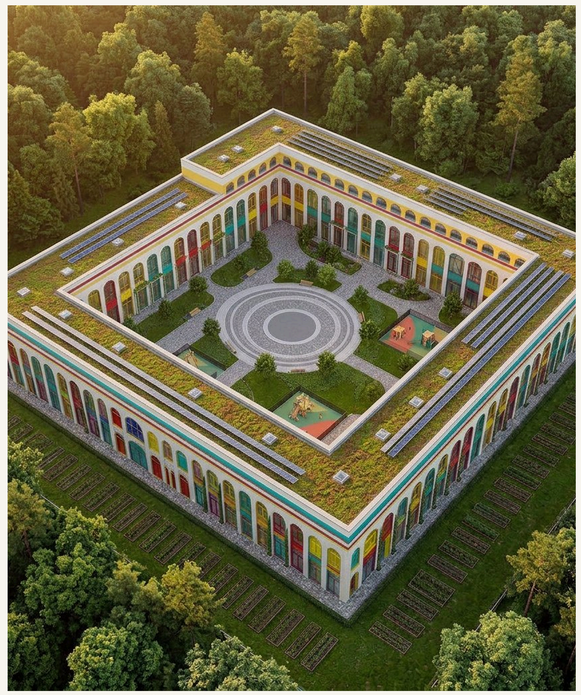

FIG. 03 — АЭРОВИД: КАРЕ, КРОВЛЯ, КОНТЕКСТ.

Что подтвердилось чертежами

Каре с защищённым двором, аркада как приём, цвет как образ, 16 площадок вокруг общей площади, бассейн в теле корпуса, пищеблок полного цикла, медблок с изолятором, 11 лестничных клеток.

● ТИПОЛОГИЯ СИЛЬНАЯ ● ЦИФРЫ ТРЕБУЮТ РЕШЕНИЯ ● КОМПЛЕКТ НЕПОЛНЫЙ

СТАТУС КОМПЛЕКТА

Есть: 7 листов АР — ПЗУ, подвал, три этажа, разрезы, фасады.

Нет: пояснительной записки, ТЭП, ведомостей, спецификаций, расчётов.

СТАДИЯ П · 013/2024-АР

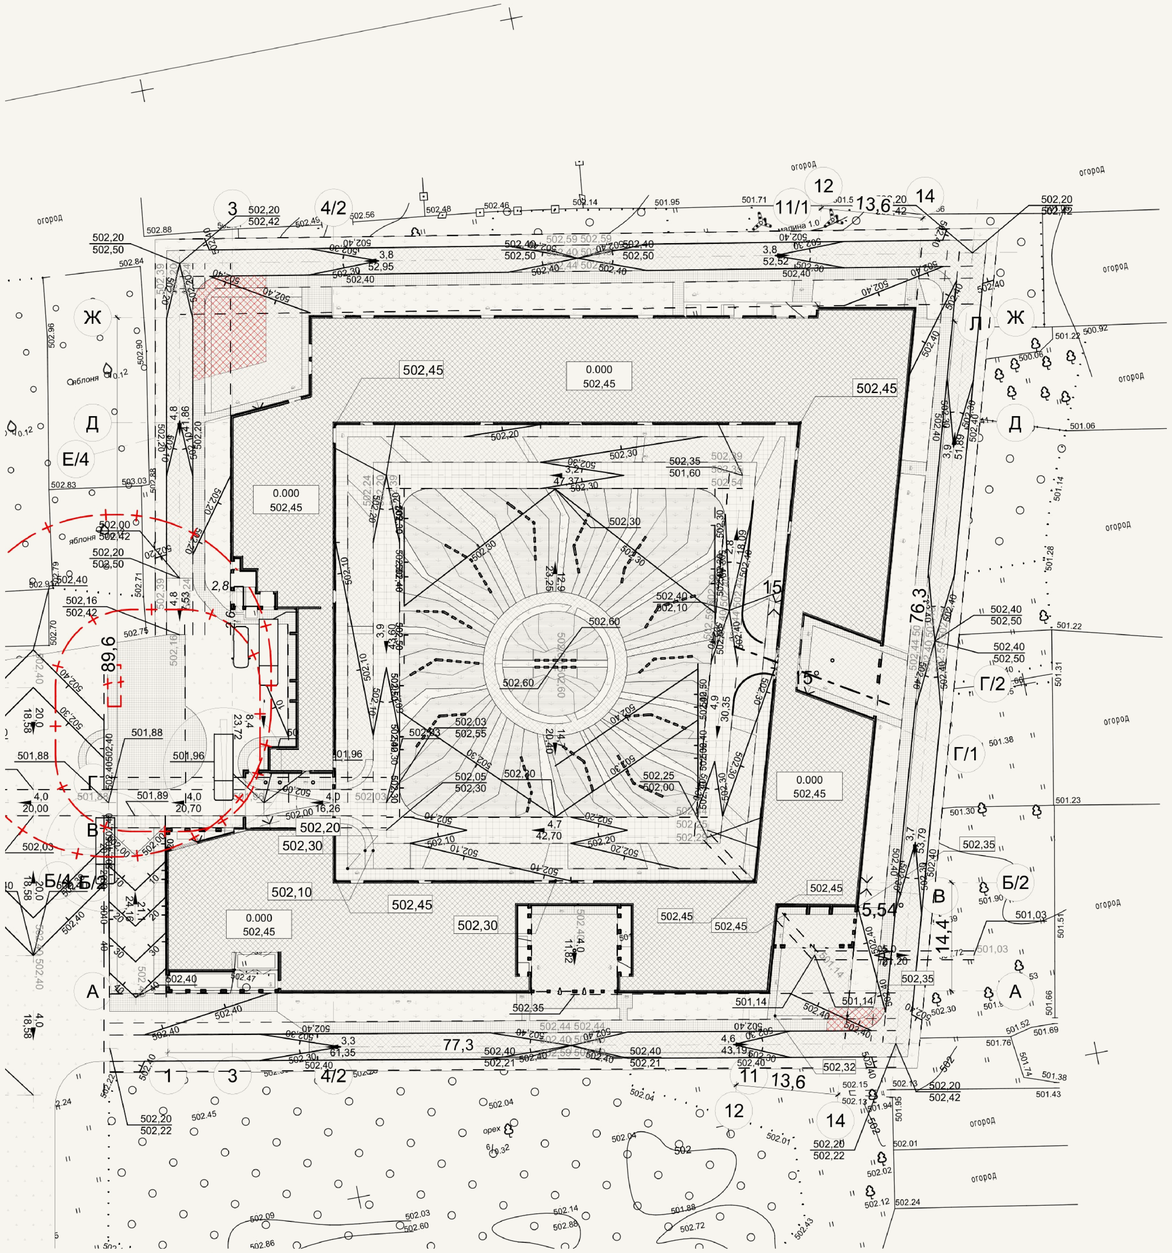

FIG. 04 — ПЗУ: КАРЕ В ЦЕНТРЕ, ФРУКТОВЫЙ САД ПО ПЕРИМЕТРУ, ВЪЕЗД С ЗАПАДА, РАЗВОРОТ ТЕХНИКИ R=8,96.

УЧАСТОК

Двор защищён, но граница открыта

С востока и юга к участку вплотную подступают частные огороды — 73 подписи «огород» на листе ПЗУ. Приватность, запахи, доступ; буферной полосы в проекте нет.

ПОКАЗАТЕЛЬ	ЗНАЧЕНИЕ
Габариты в осях	89,61 × 77,30 м
Пятно застройки	≈ 3 000 м²
Двор	≈ 3 900 м²
Площадки	1 970 м² / 16
Деревья по ведомости	15 шт
Машиноместа	**0**

FIG. 05 — УЧАСТОК В КОНТЕКСТЕ ЛЕСА И ЧАСТНОГО СЕКТОРА: БУФЕРНОЙ ПОЛОСЫ НЕТ.

ВЪЕЗД И РАЗВОРОТ

Один въезд с запада, разворотная площадка R=8,96 у служебного корпуса. Второго выезда и круга для пожарной техники 12 × 12 м нет.

ОЗЕЛЕНЕНИЕ

15 деревьев по ведомости на 1,45 га: орех 6, яблоня 5, шелковица 4. Для участка такого размера это 10 деревьев на гектар при норме 80–120.

ГРАНИЦА

Ограждение по периметру есть, но с востока и юга оно идёт вплотную к частным огородам. Нужен отступ 3–5 м и двухрядная посадка.

1,45 га
ПЛОЩАДЬ УЧАСТКА

21 %
ЗАСТРОЙКА

27 %
ДВОР

52 %
ПРОЕЗДЫ И БУФЕР

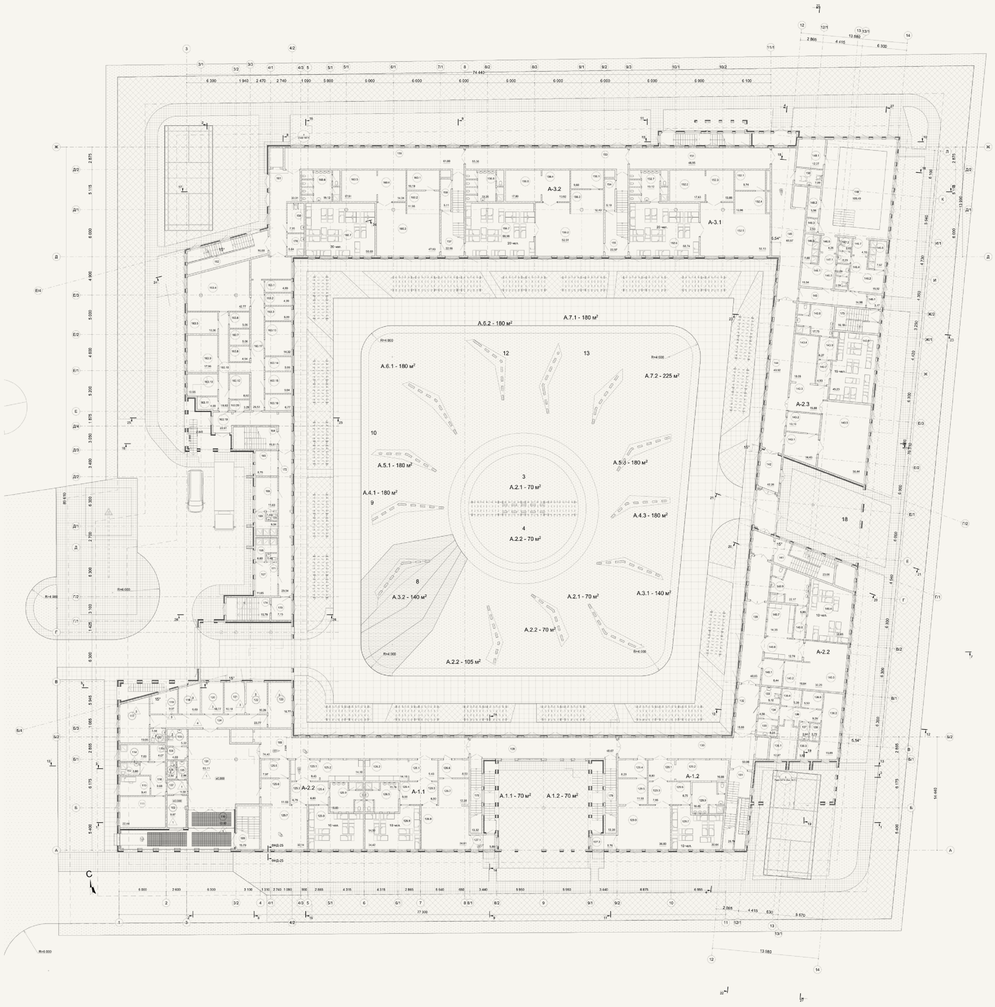

FIG. 06 — 1 ЭТАЖ: 6 ГРУПП, ПИЩЕБЛОК, МЕДБЛОК, АДМИНИСТРАЦИЯ, БАССЕЙН. ДВОР С 16 ПЛОЩАДКАМИ.

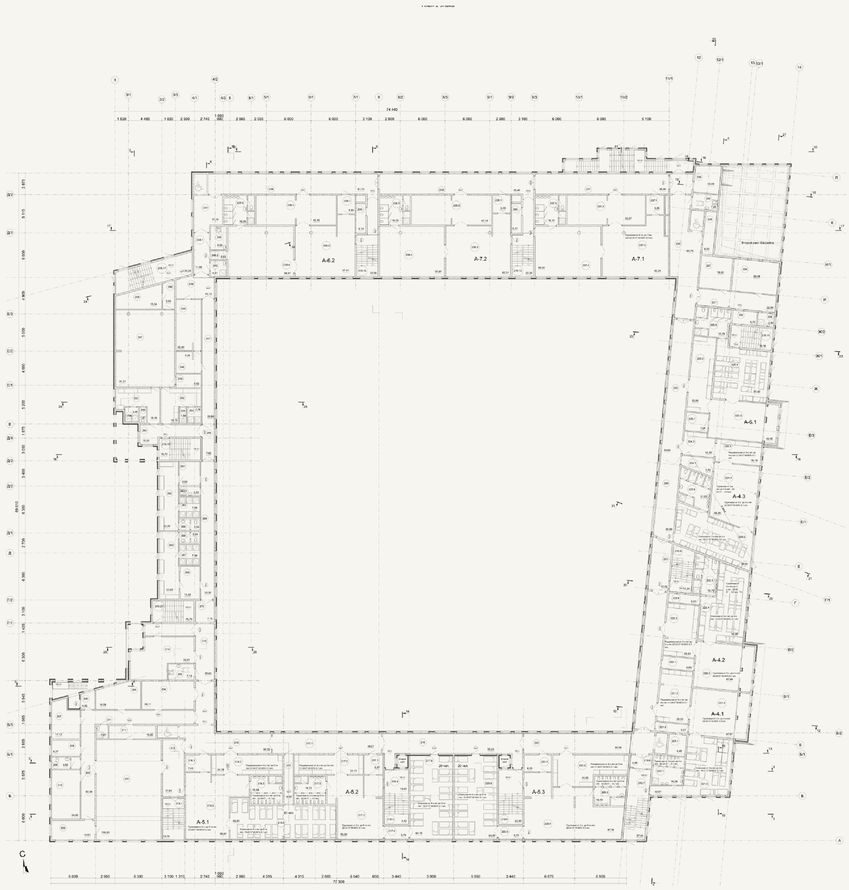

FIG. 07 — 2 ЭТАЖ: 10 ГРУПП, МУЗКЛАСС 116 М², ФИЗЗАЛ И КРУЖКОВЫЙ ЗАЛ С ПУИ.

FIG. 08 — 3 ЭТАЖ: СПОРТПЛОЩАДКИ НА КРОВЛЕ, ТЕРРАСА, ТЕХПОМЕЩЕНИЯ.

Площади по этажам

ЭТАЖ	М²	ГРУПП
Подвал −3,300	2 373,0	—
1 этаж ±0,000	2 986,3	6
2 этаж +4,500	3 412,8	10
3 этаж +8,500	1 079,8	—
Итого	**9 852,0**	**16**

16 ГРУПП · 11 ЛК · 2× МГН

ПЛОЩАДИ, М² — СРАВНЕНИЕ С ДВОРОМ

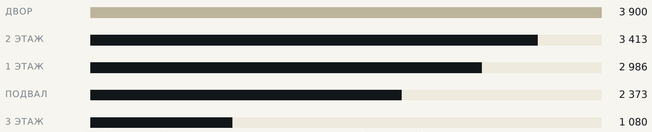

Суммарно 9 852 м², из них 2 373 м² — подвал. Двор по площади больше любого этажа, кроме второго.

Что видно на планах

16 групповых ячеек полного состава: раздевальная детей и взрослых, буфет, место кормления, спальня, туалетная, пеленальная у ясельных. 11 лестничных клеток, зоны МГН на каждом этаже. Пищеблок полного цикла с девятью цехами, медблок с изолятором, бассейн с трибунами.

ЧТО ТРЕБУЕТ ОТВЕТА

2 этаж больше 1-го на 426 м² — без объяснения. Открытые площадки 3 этажа (374,7 м²) включены в площадь этажа. «Второй свет бассейна» — без площади.

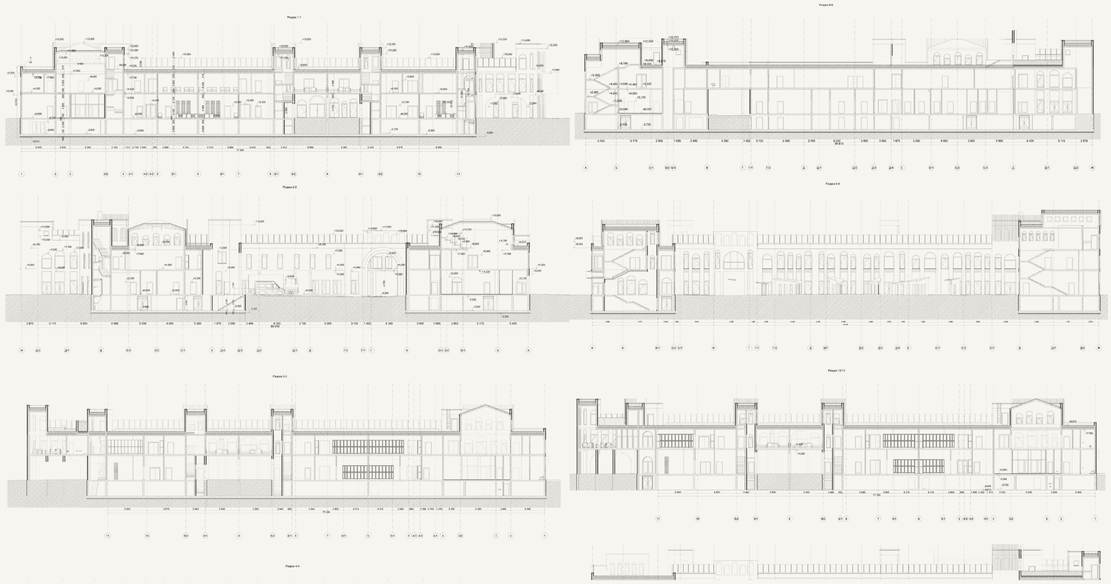

FIG. 09 — ШЕСТЬ РАЗРЕЗОВ: ДВА ЭТАЖА, ТРЕТИЙ ЧАСТИЧНЫЙ, ПОДВАЛ НА ВСЮ ШИРИНУ КОРПУСА.

ВЕРТИКАЛЬ

Два этажа по 4,5 м и кровля как пятый фасад

Бассейн двусветный, со световым фонарём. На +8,50 — спортплощадки и терраса; парапет +12,000…+13,200.

ОТМЕТКА	ЧТО НА НЕЙ
−3,300	подвал, техпомещения
±0,000	1 этаж, входы
+4,500	2 этаж, группы
+8,500	3 этаж, площадки
+13,200	парапет, максимум

РАЗРЕЗ 3-3

Бассейн в два света, световой фонарь, трибуны на 2 этаже.

РАЗРЕЗ 13-13

Кровля с перепадом +8,50 / +11,20 и парапетом +13,20.

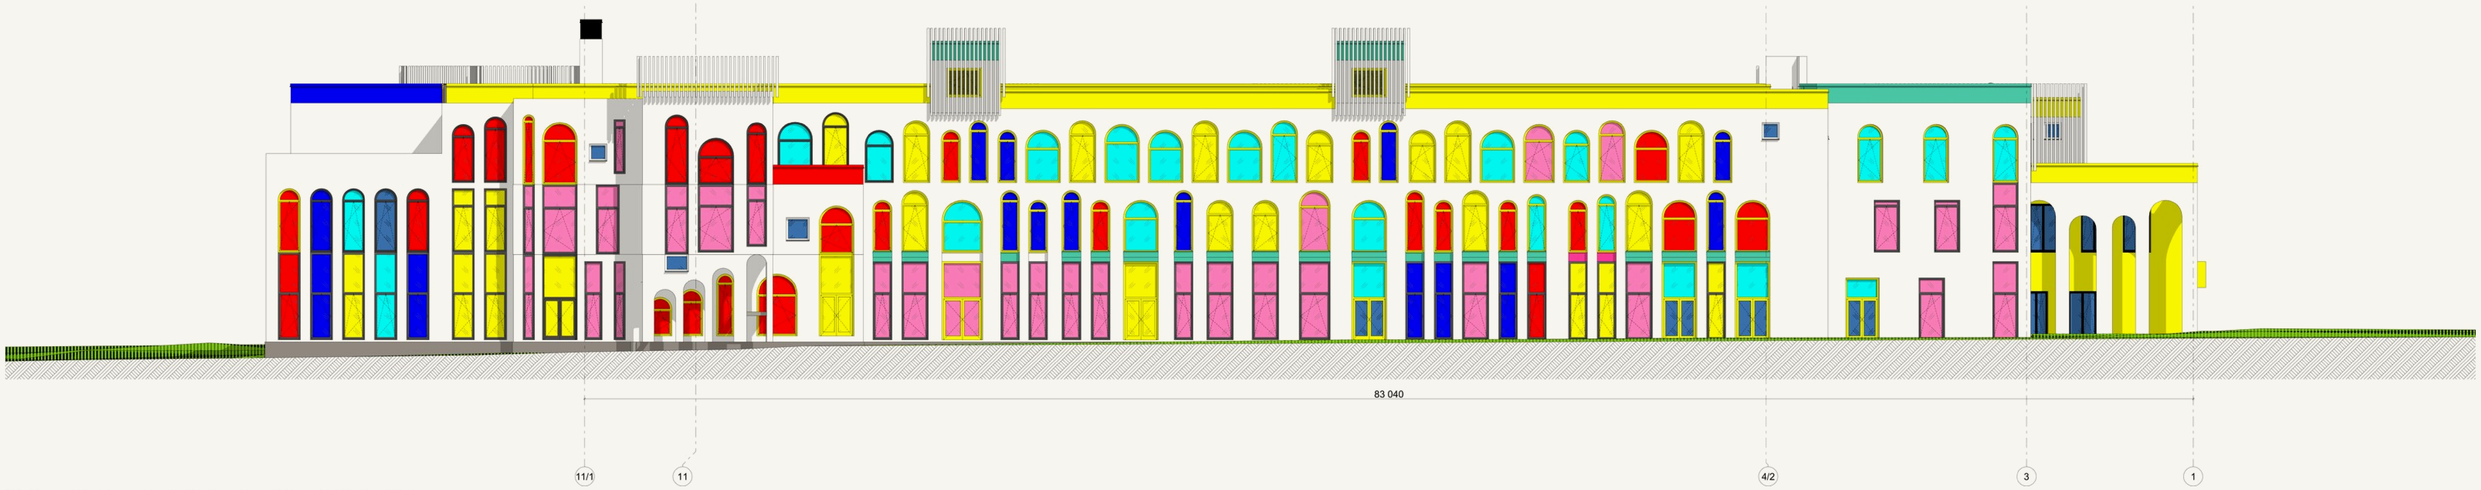

FIG. 10 — ФАСАД 11/1-1, 83 040 ММ: ДВА ЯРУСА АРОК, СПЛОШНАЯ ЦВЕТНАЯ ЗАЛИВКА.

FIG. 11 — ФАСАД Ж-А, 89 610 ММ: ГЛАВНЫЙ ВХОД, НАВЕСЫ, ЗОНА ЗАГРУЗКИ.

ДЕТСКИЙ САД НА УЛ. КОЛЛЕКТИВНАЯ · ПЯТИГОРСК · 013/2024-АР

СРЕДА

Двор как внешняя комната каждой группы

Круглая площадь в центре — амфитеатр, линейка, праздник. Вокруг шестнадцать площадок, у каждой свой выход из групповой.

Двор защищён кольцом корпусов: посторонний не входит, ребёнок не выходит. Это главное достоинство схемы.

ПЛОЩАДКИ ПО ГРУППАМ, М²

А-7.2	225	14,1 / реб.
А-5.1 · А-6.1 · А-6.2 · А-5.3 · А-4.3	180	9,0
А-3.1 · А-3.2	140	14,0 / 7,0
А-2.2	105	10,5
А-1.1 · А-1.2 · А-2.1 · А-2.2 · А-2.3	70	7,0 / 3,5

Дефицит к ориентиру 180 м² — около 30 %; выравнивается за счёт кровли и перераспределения.

3 900 м²
ДВОР

1 970 м²
ПЛОЩАДКИ

123 м²
НА ГРУППУ

15
ДЕРЕВЬЕВ

FIG. 12 — ЭТАЛОННЫЙ КАДР: ПЛОЩАДКА ГРУППЫ 180 М², ОГРАЖДЕНИЕ 1,1 М, ОБОРУДОВАНИЕ 2,5–3 М, ПЯТНАДЦАТЬ ДЕРЕВЬЕВ ВО ДВОРЕ. ЭТОТ МАСШТАБ И ДЕРЖИМ ВО ВСЕХ ОСТАЛЬНЫХ КАДРАХ.

FIG. 13 — ДВОР И КРЫШИ СВЕРХУ: КУРТ, РАДИАЛЬНЫЕ ДОРОЖКИ, ПЯТНАДЦАТЬ ДЕРЕВЬЕВ.

FIG. 14 — ВЕЧЕРНИЙ СЦЕНАРИЙ: ТОТ ЖЕ МАСШТАБ, ДРУГАЯ ТЕМПЕРАТУРА СВЕТА.

ДЕТСКИЙ САД НА 12 ГРУПП · КОЛЛЕКТИВНАЯ · ПЯТИГОРСК · 013/2024-АР

FIG. 15 — ПЛАН 3 ЭТАЖА: ТРИ ОТКРЫТЫЕ СПОРТПЛОЩАДКИ 176,3 М², ТЕРРАСА 198,4 М², ХУДКЛАСС.

ПЯТЫЙ ФАСАД

Кровля, которой нет на картинках

Ни зелёной кровли, ни солнечных панелей в стадии П нет. На +8,50 — открытые спортплощадки старших групп и терраса. Решение требует расчёта эвакуации, ограждений 1,2 м и регламента доступа.

ЭЛЕМЕНТ	ПЛОЩАДЬ / СТАТУС
Спортплощадки ×3	176,3 м²
Терраса	198,4 м²
Художественный класс	40,2 м²
Всего открытых зон на +8,50	375 м² / 19 %
Ограждение кровли	**не задано**
Расчёт эвакуации	**отсутствует**
Зелёная кровля в проекте	**0**
Солнечные панели в проекте	**0**

Открытые площадки на кровле — не ошибка, а сознательное решение: в условиях плотной застройки двор не вмещает весь набор. Вопрос лишь в том, как обеспечить безопасность и эвакуацию.

Три варианта

А. Оставить открытыми: расчёт эвакуации, ограждение 1,2 м с поручнем, ветрозащита, регламент выхода.

Б (рекомендуется). Закрыть светопрозрачным навесом: функция сохраняется, дети не на парапете, эксплуатация дешевле.

В. Отказаться от третьего этажа: получить зелёную кровлю и СЭС — то, что обещают визуализации.

А · ОТКРЫТО В · НАВЕС С · ЗЕЛЁНАЯ КРОВЛЯ

ВЫВОД

Кровля — единственное место, где проект обещает больше, чем рисует. Решение о ней определяет и смету, и образ.

FIG. 16 — «ЗЕЛЁНАЯ КРОВЛЯ» С ВИЗУАЛИЗАЦИИ: В ПРОЕКТЕ ОТСУТСТВУЕТ. ОБЕЩАННОЕ И ЗАПРОЕКТИРОВАННОЕ НУЖНО СВЕСТИ К ОДНОМУ РЕШЕНИЮ.

Разбор идёт от экспертизы к образу

Пять пунктов блокируют прохождение, девять бьют по качеству и смете, четыре — по оформлению. Ни один не требует переделки архитектуры: правятся данные, состав и палитра.

18 ЗАМЕЧАНИЙ · **10** ДЕЙСТВИЙ · **4** РЕШЕНИЯ

A · БЛОКИРУЕТ ЭКСПЕРТИЗУ
Состав и данные

01 Комплект — только чертежи
Нет пояснительной записки, ТЭП, ведомостей и спецификаций. По ПП № 87 стадия П включает текстовую часть.
Действие: ПЗ 40–60 стр. и свод ТЭП.

02 Вместимость не зафиксирована
16 групп, подписи 10–20 детей. 9 852 м² дают 41 м²/место при ориентире 12–15 — либо мест больше, либо площади завышены.
Действие: принять одно число в задании.

03 Штампы и подписи
В основной надписи «#Название Организации»; нет подписей ГИПа и главного архитектора, нет согласований и заданий смежников.
Действие: заполнить штамп, приложить задания.

04 Дети на кровле 3 этажа
Спортплощадки и терраса на +8,50 без расчёта эвакуации, ограждений и ветрозащиты.
Действие: раздел ПБ, ограждение 1,2 м с поручнем.

08 Парковки нет вообще
Ни машиноместа, ни drop-off. Разворот R=8,96 меньше площадки 12 × 12 м для пожарной техники.
Действие: карман на 4–5 машин, 15–20 м/м.

15 Дубли номеров помещений
150 · 221.2 · 222.1 · 250 идут дважды с разными площадями; 149.1 без наименования.
Действие: сквозная нумерация и сверка.

41 м²/место
ПРИ ОРИЕНТИРЕ 12–15

B · КАЧЕСТВО И СМЕТА
Планировка и среда

06 Групповые от 70 до 225 м²
Разброс в три раза. При норме 2,5 м²/ребёнок групповая на 20 детей — 50 м², то есть запас до 3,6×.
Действие: площади по программе групп.

07 Площадок на 30 % меньше нормы
1 970 м² на 16 групп = 123 м²/группа при ориентире 180. Хуже всего А-3.2: 7,0 м²/ребёнок.
Действие: перебалансировать двор и кровлю.

09 15 деревьев на 3 900 м²
Орех 6 · яблоня 5 · шелковица 4. Тени почти нет; орех у игровых зон — аллергия и корневая.
Действие: +15–20 крупномеров, орех в буфер.

10 Огороды вплотную к границе
73 подписи «огород»: приватность, пестициды, животные, доступ. Буферной полосы нет.
Действие: буфер 3–5 м и два ряда посадки.

17–18 Площади посчитаны неверно
Открытые площадки включены в площадь 3 этажа — 374,7 из 1 079,8; 2 этаж больше 1-го на 426 м².
Действие: разделить площадь этажа и кровли.

05 Площадки на кровле не равны дворовым
Спортплощадки на +8,50 засчитаны в нормативный набор, но не могут заменить прогулочные площадки у групп: доступ по лестнице, ветер, эвакуация.
Действие: считать их дополнительной, а не основной площадью.

123 м²/группа
ПРИ ОРИЕНТИРЕ 180

C · ОБРАЗ И ОФОРМЛЕНИЕ
Фасад и документ

11 Девять чистых RGB-цветов
38 заливок на листе. Цвет не привязан к функции, чистые тона выгорают, в RAL аналогов нет.
Действие: 6 цветов RAL, правило 80 / 15 / 5.

12 Одна арка на всё
Вход в группу не отличается от окна группы. Первый этаж читается как торговая галерея.
Действие: три типа проёма в сетке 6,3 м.

13 Главный вход не читается
Нет козырька, увеличенного тамбура, места ожидания и навигации.
Действие: вынести объём входа на 2,5–3 м.

14 На фасадах нет инженерии
Ни вентрешёток, ни водосточных воронок, ни молниезащиты, ни камер, ни освещения. Всё это появится в Р и разрушит цветную графику.
Действие: показать инженерию уже в П.

16 Опечатки в наименованиях
«Зал басейна», «Груповая», «Художественый», «постирочная» без пом. — документ читается как рабочий черновик.
Действие: корректура и нормоконтроль.

38 заливок
ИЗ НИХ 9 ЧИСТЫХ RGB

ЧТО В ПРОЕКТЕ УЖЕ СИЛЬНО — ЭТО НЕ ТРОГАЕМ
КАРЕ И ДВОР · 16 ПЛОЩАДОК · БАССЕЙН · ПИЩЕБЛОК · МЕДБЛОК · 11 ЛК

ПАЛИТРА ФАСАДОВ ИЗ PDF — 38 ЗАЛИВОК, ИЗ НИХ 9 ЧИСТЫХ → 6 RAL

FFFF00	FF0000	00FFFF	0000FF	87D220	FF80C0	FF9E3E	50CBAC	09F2A0

Что делать и в каком порядке

Десять правок разной цены. Первые две не требуют решений — их можно делать сразу, параллельно с обсуждением остальных.

СРОК · СТОИМОСТЬ

01 Почистить экспликации
Дубли номеров, наименования, опечатки. Самое дешёвое и заметное исправление.
1–2 НЕДЕЛИ · НИЗКАЯ

02 Свести ТЭП и баланс
Площадь застройки, двор, площадки, озеленение, места, вместимость — одним листом.
2–3 НЕДЕЛИ · НИЗКАЯ

03 Зафиксировать вместимость
240 / 300 / 320 мест. Без этого любая правка площадей — переделка.
3–6 НЕДЕЛЬ · РЕШЕНИЕ

04 Решить судьбу 3 этажа
Открыто / навес / отказ в пользу зелёной кровли.
3–6 НЕДЕЛЬ · СРЕДНЯЯ

05 Найти парковку
Drop-off 4–5 машин, 15–20 м/м, разворот 12 × 12 м.
3–6 НЕДЕЛЬ · СРЕДНЯЯ

06 Перебалансировать двор
Старшим группам +180 м², +15–20 крупномеров, перголы, орех в буфер.
3–6 НЕДЕЛЬ · СРЕДНЯЯ

07 Переписать палитру
6 цветов RAL, 80 / 15 / 5, цвет = возраст группы. Замена ведомости отделки.
4–8 НЕДЕЛЬ · 2–3 ЛИСТА

08 Ввести три типа проёма
Окно 2,1 · вход 1,8 · общий блок 3,0 м в сетке 6,3 м.
4–8 НЕДЕЛЬ · 2–3 ЛИСТА

09 Кровля: считать или убрать
Седаум 60–80 кг/м², панели 15–20, доступ — либо честно снять с визуализаций.
6–10 НЕДЕЛЬ · ВЫСОКАЯ

10 Пересобрать визуализации
Шесть канонических кадров по пяти схемам вместо восьми случайных.
2 НЕДЕЛИ · НИЗКАЯ

ГРАФИК: 12 НЕДЕЛЬ, РАБОТЫ ИДУТ ПАРАЛЛЕЛЬНО

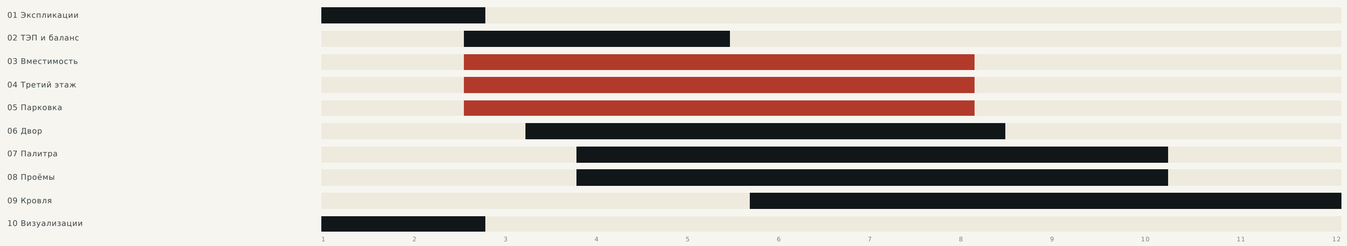

ЧТО ГОТОВО УЖЕ СЕЙЧАС

Пять схем раздела 04 аудита можно показывать вместо текущих визуализаций: они совпадают с проектом по габаритам, сетке, отметкам и составу помещений. Это честная подача — и она выигрывает у красивых картинок, которые не сходятся с чертежами.

FIG. 17 — ОБРАЗ СОХРАНЯЕТСЯ: МЕНЯЮТСЯ ЦИФРЫ, А НЕ АРХИТЕКТУРА.

№	РЕШЕНИЕ ЗАКАЗЧИКА	ВАРИАНТЫ
1	Вместимость	240 / 300 / 320
2	Третий этаж	открыто / навес / отказ
3	Парковка	участок / drop-off
4	Зелёная кровля и СЭС	в стадии Р / убрать

Ближайший шаг

Согласовать четыре решения на этой неделе — и выпустить восьмой лист: ТЭП и баланс территории. Дальше правки идут пакетами, без перерисовки чертежей.

СМОТРЕТЬ АУДИТ → · 5 СХЕМ · 6 КАДРОВ